


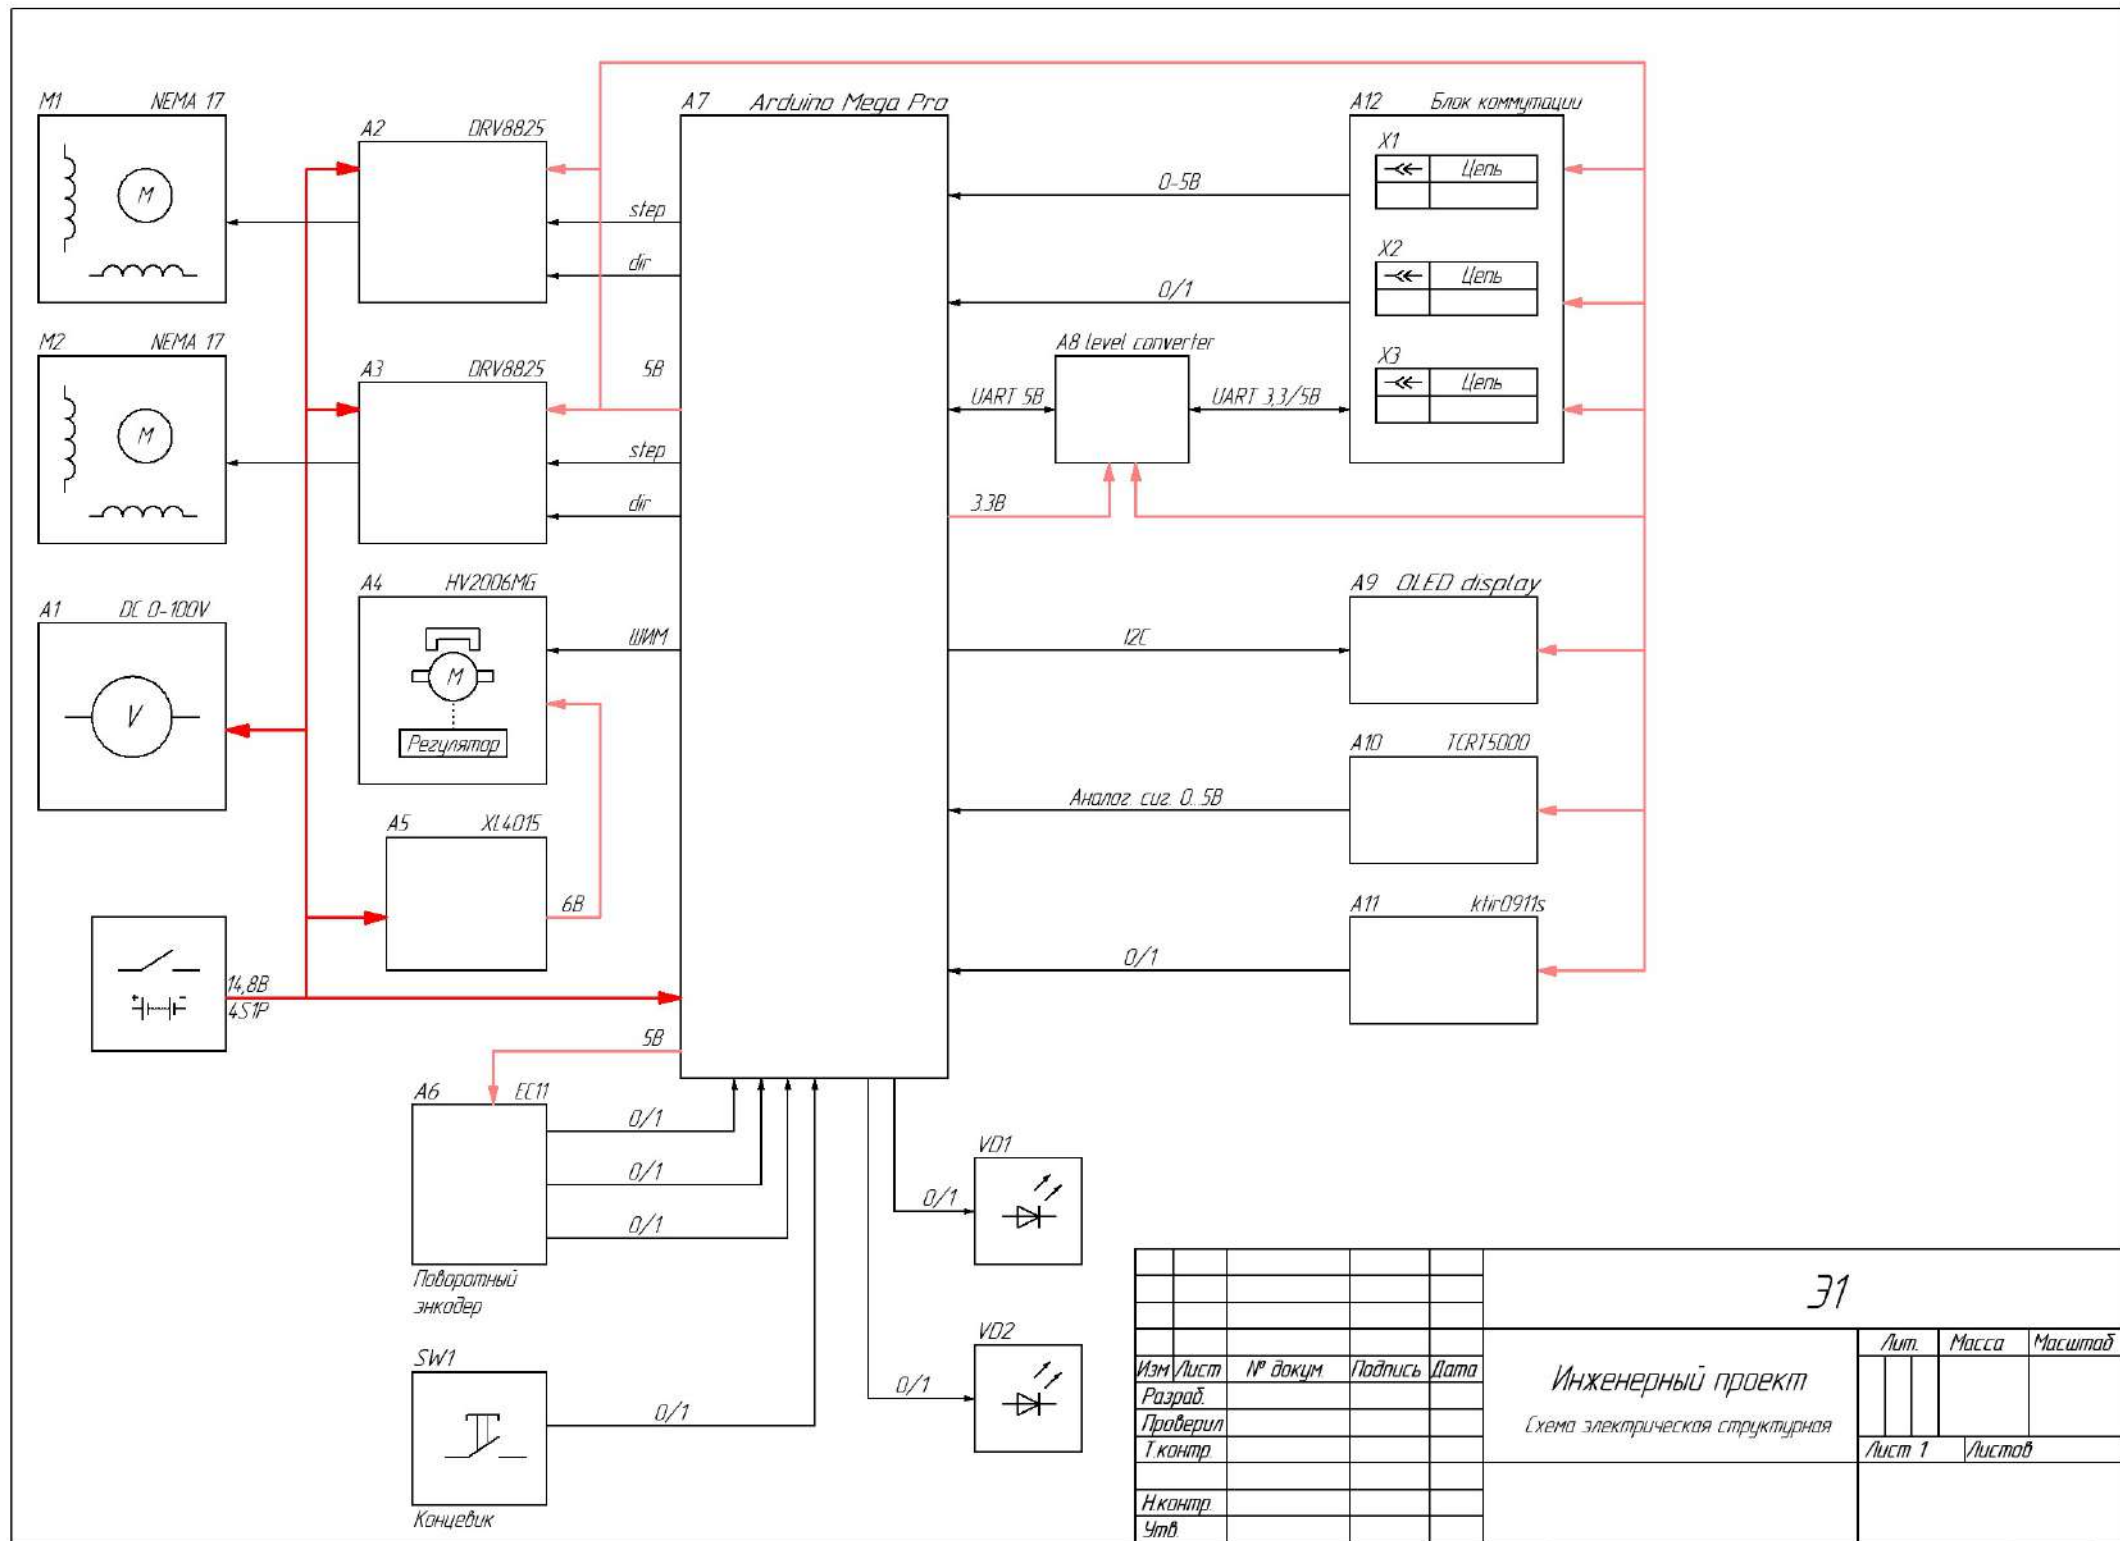

					31			
Изм/лист	№ докум	Подпись	Дата		Инженерный проект			
Разраб								
Проверил					Схема электрическая структурная			
Т. контр								
Н. контр					Лист 1 / Листов			
Утв								