


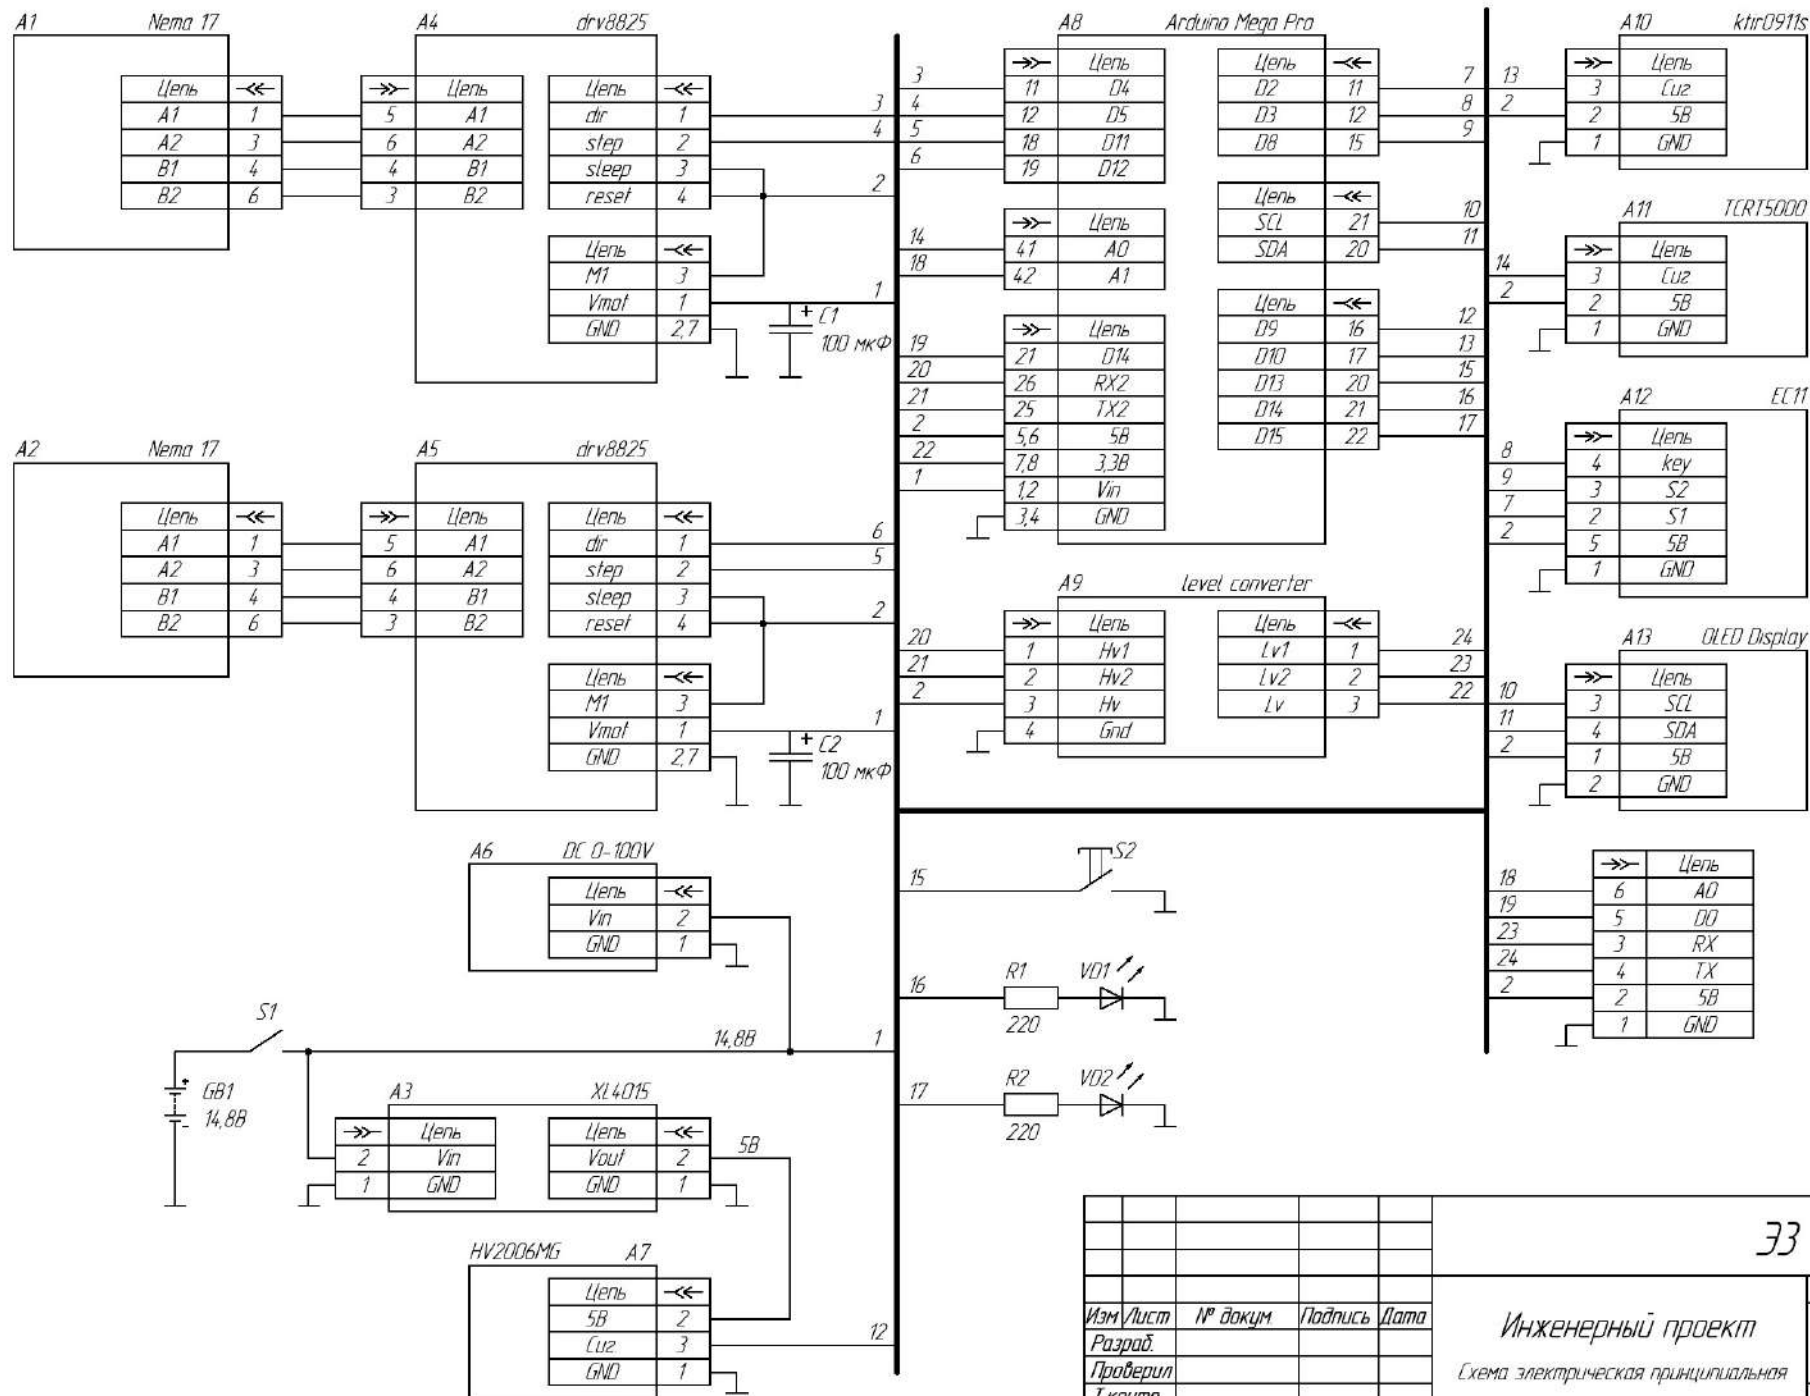

				33		
Изм./лист	№ докум	Подпись	Дата	Инженерный проект		
Разработ						
Проверил				Схема электрическая принципиальная		
Т. контр						
Н. контр				Лист 1 / Листов		
Умб						