


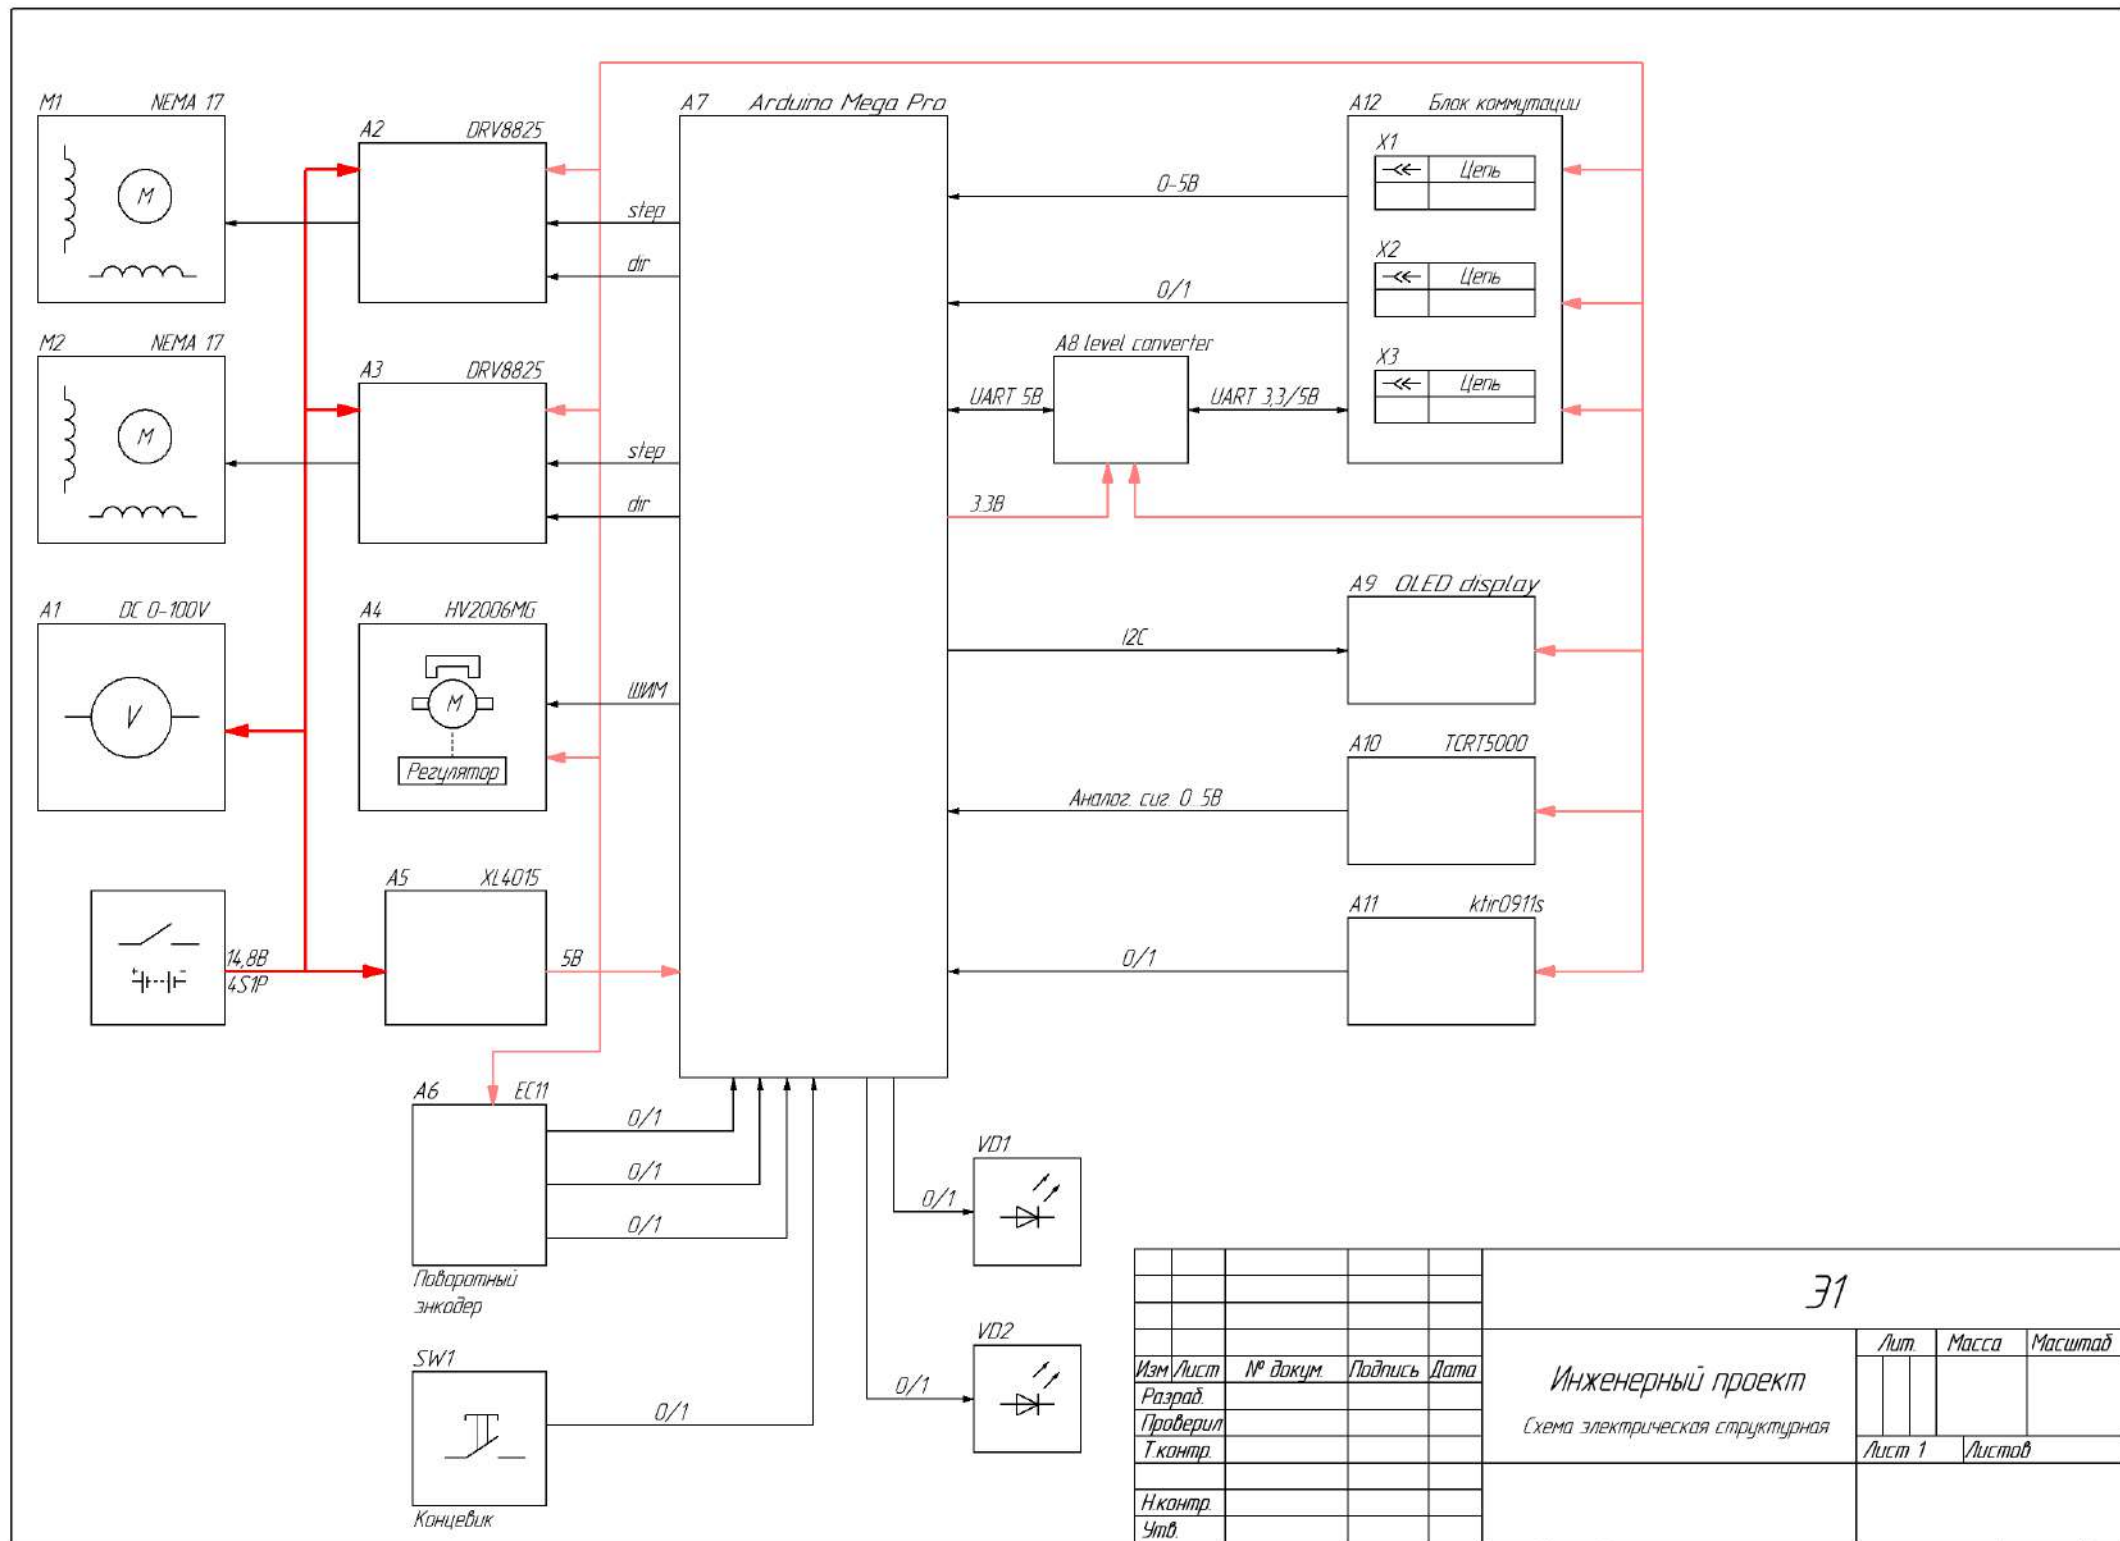

						31			
Изм/лист	№ докум	Подпись	Дата	Инженерный проект		Лит.	Масса	Масштаб	
Разраб.									
Проверил				Схема электрическая структурная		Лист 1			
Т контр.						Листов			
Нконтр									
Утв									