


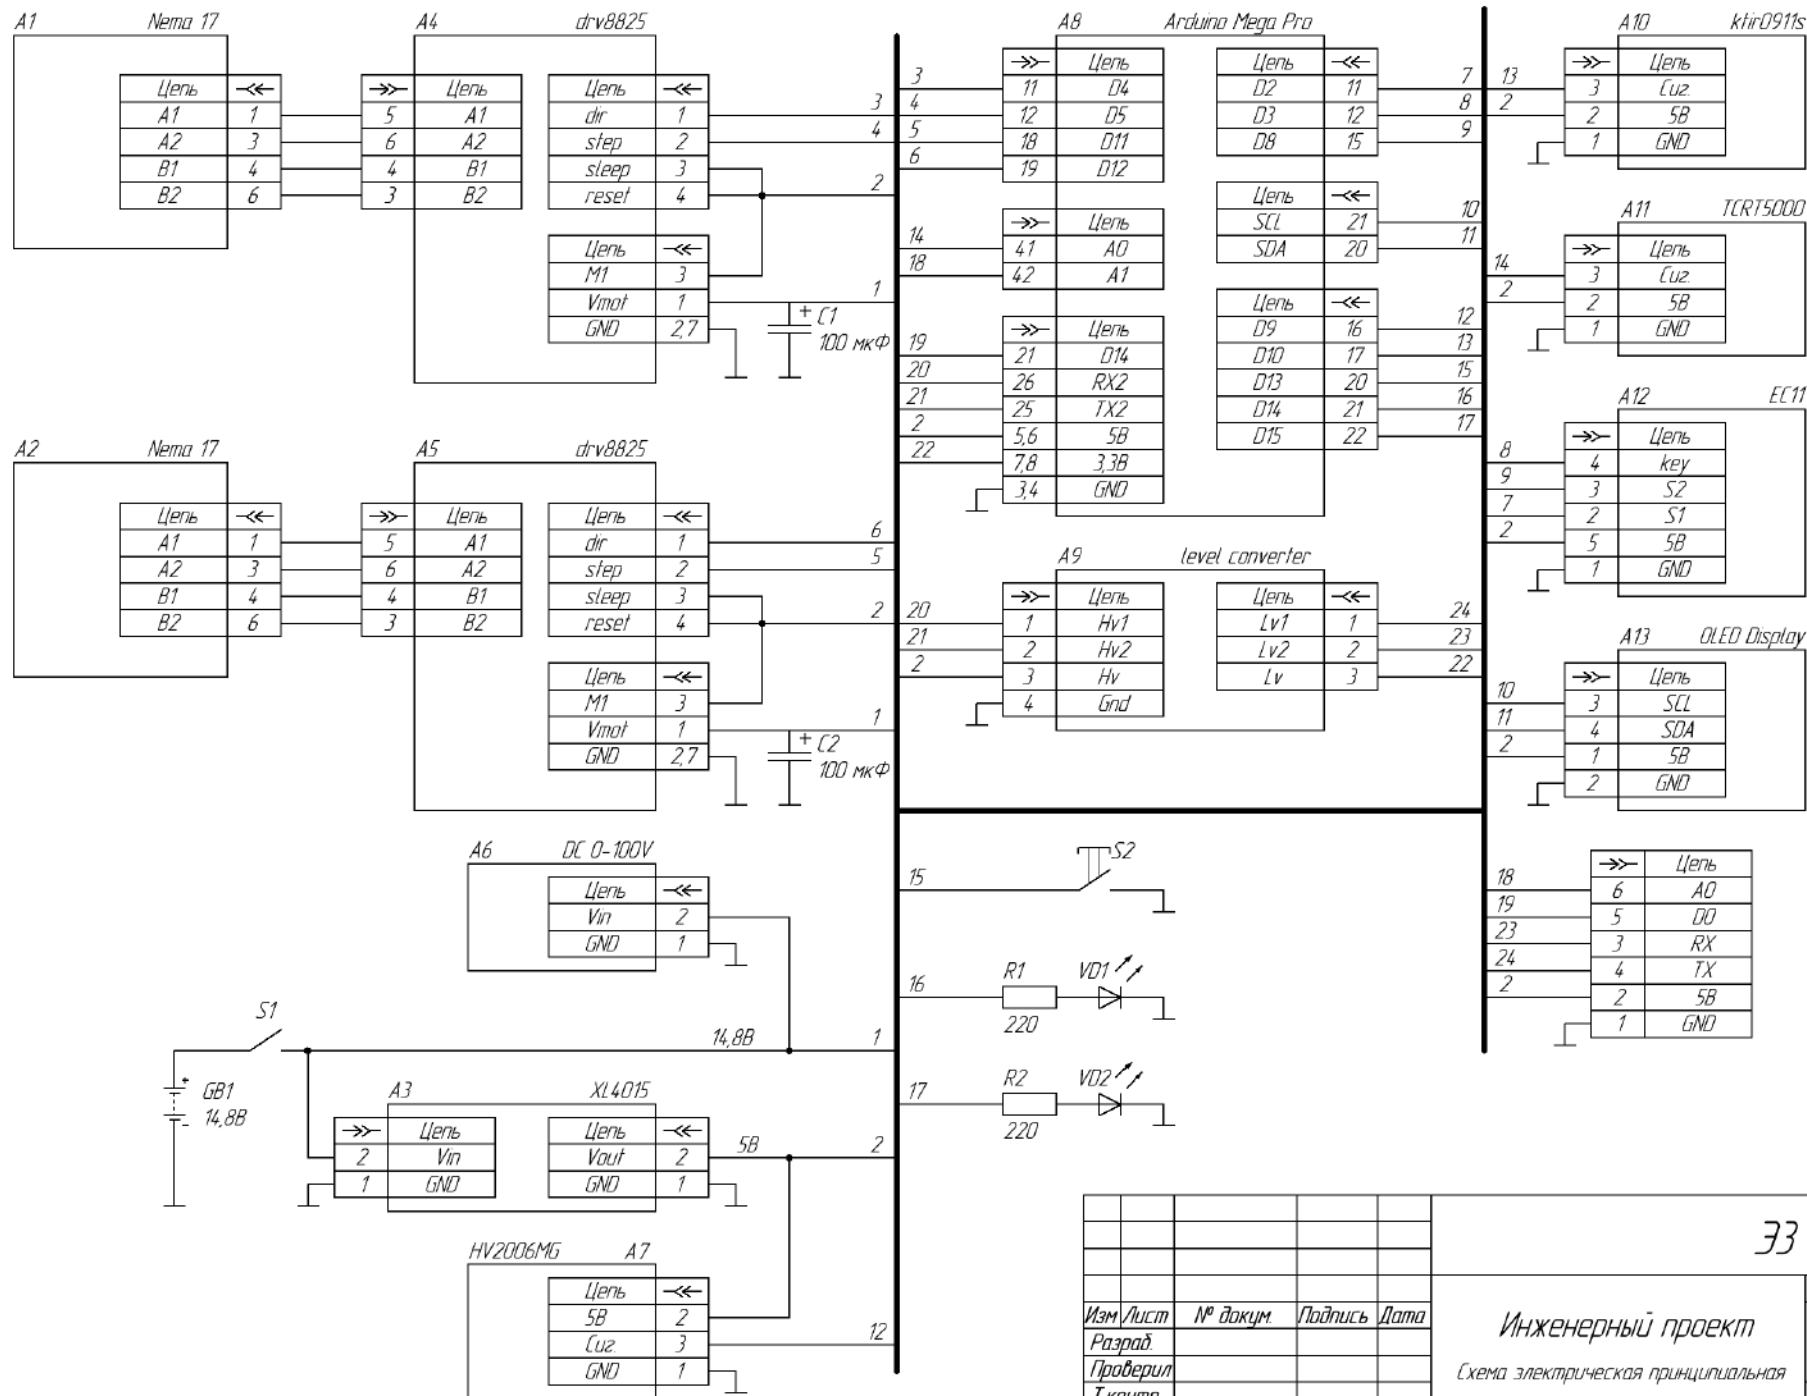

				33				
Изм./лист	№ докум.	Подпись	Дата	Инженерный проект		Лит.	Масса	Масштаб
Разраб.								
Проверил				Схема электрическая принципиальная		Лист 1 / Листов		
Т.контр.								
Н.контр.								
Умб.								